



BURSA ULUDAĞ ÜNİVERSİTESİ ZİRAAT FAKÜLTESİ
PEYZAJ MİMARLIĞI BÖLÜMÜ



PEYZAJ PROJESİ 5 - GEMLİK KIYI PROJESİ
FİNAL TESLİM

DERS YÜRÜTÜCÜSÜ: Arş.Gör.Dr. OSMAN ZEYBEK


MİRZA DUGOPOLJAC
052295047
26.06.26

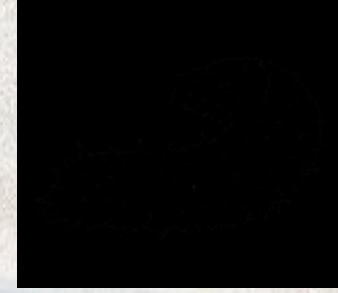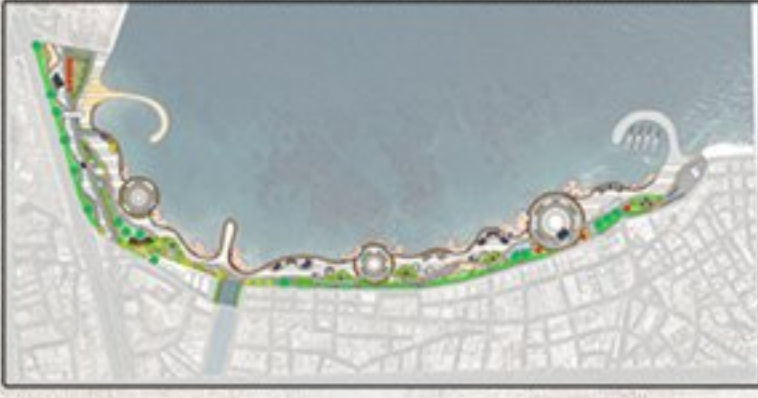

TEMA - KONSEPT Maruziyet - Deniz Hiyarı


Gemlik kıyısı; rüzgâr, dalga, tuzluluk, insan kullanımı, kirlilik, müsilaj ve zaman gibi sürekli etkilere maruz kalan dinamik bir kıyı alanıdır. Deniz hıyarı konseptiyle bu maruziyetler, yalnızca bir baskı unsuru olarak değil; görünür kılınan, işlenen ve kamusal deneyime dönüştürülen bir tasarım yaklaşımı olarak ele alınmıştır.

BURSA ULUDAĞ ÜNİVERSİTESİ ZİRAAT FAKÜLTESİ PEYZAJ MİMARLIĞI BÖLÜMÜ
PEYZAJ PROJESİ 5 - GEMLİK KIYI PROJESİ BİTKİSEL PAFTA
FİNAL TESLİMİ

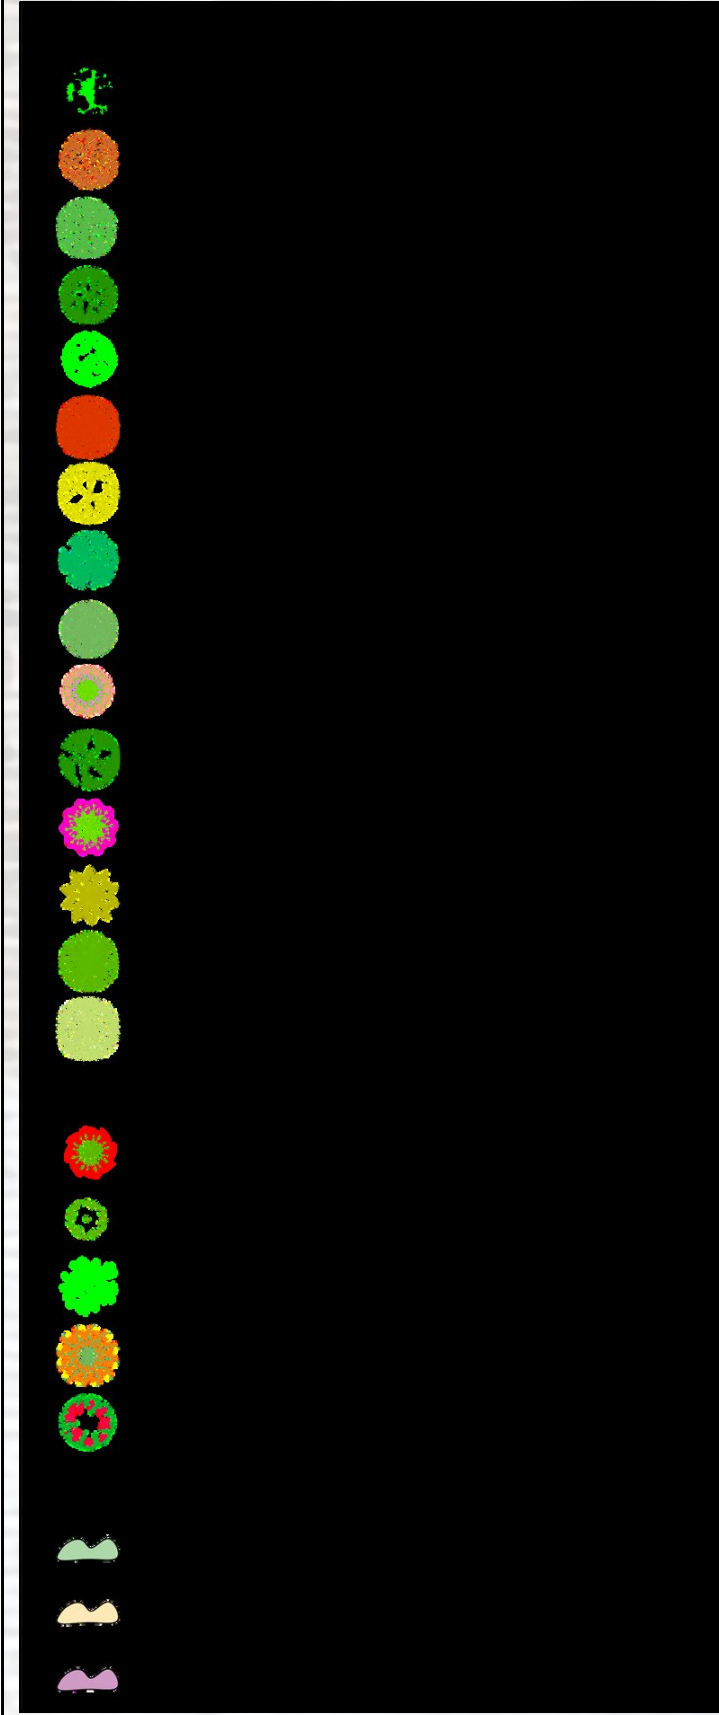

MİRZA DUGOPOLJAC
052295047
1/2000 ÖLÇEK
26.06.26

BURSA ULUDAĞ ÜNİVERSİTESİ ZİRAAT FAKÜLTESİ PEYZAJ MİMARLIĞI BÖLÜMÜ
PEYZAJ PROJESİ 5 - GEMLİK KIYI PROJESİ YAPISAL PAFTA
FİNAL TESLİMİ

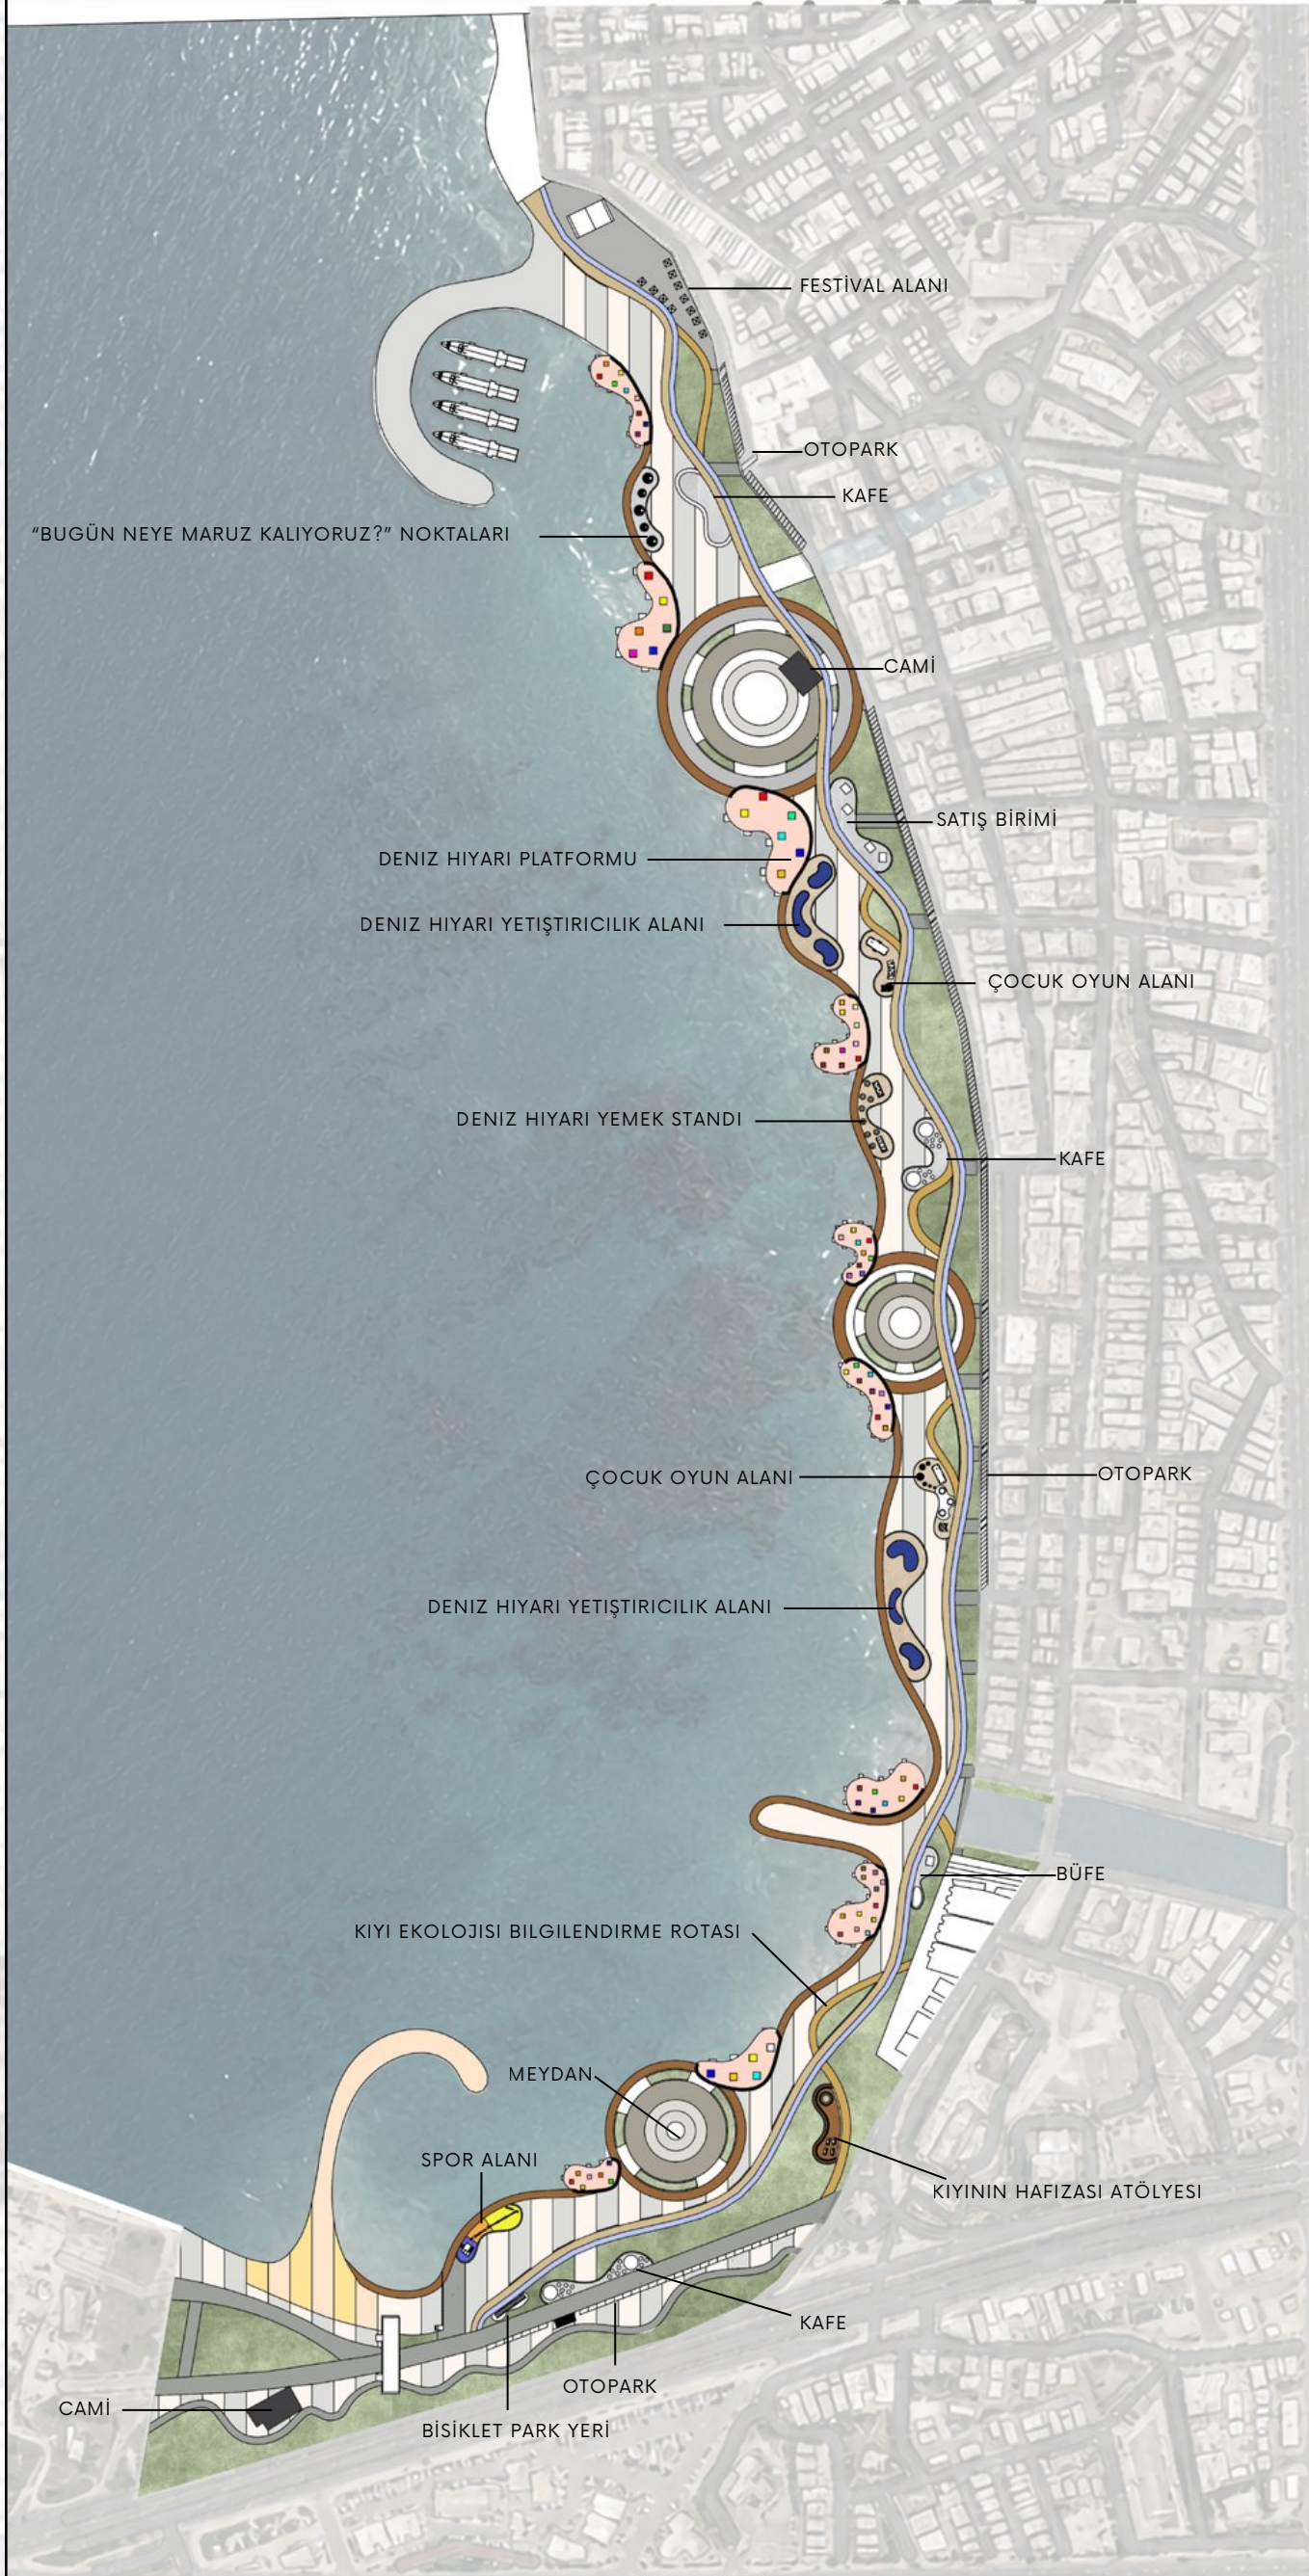

A - KESİT



B- KESİT




C - KESİT



GENÇLİK ZONU



HAREKET ZONU

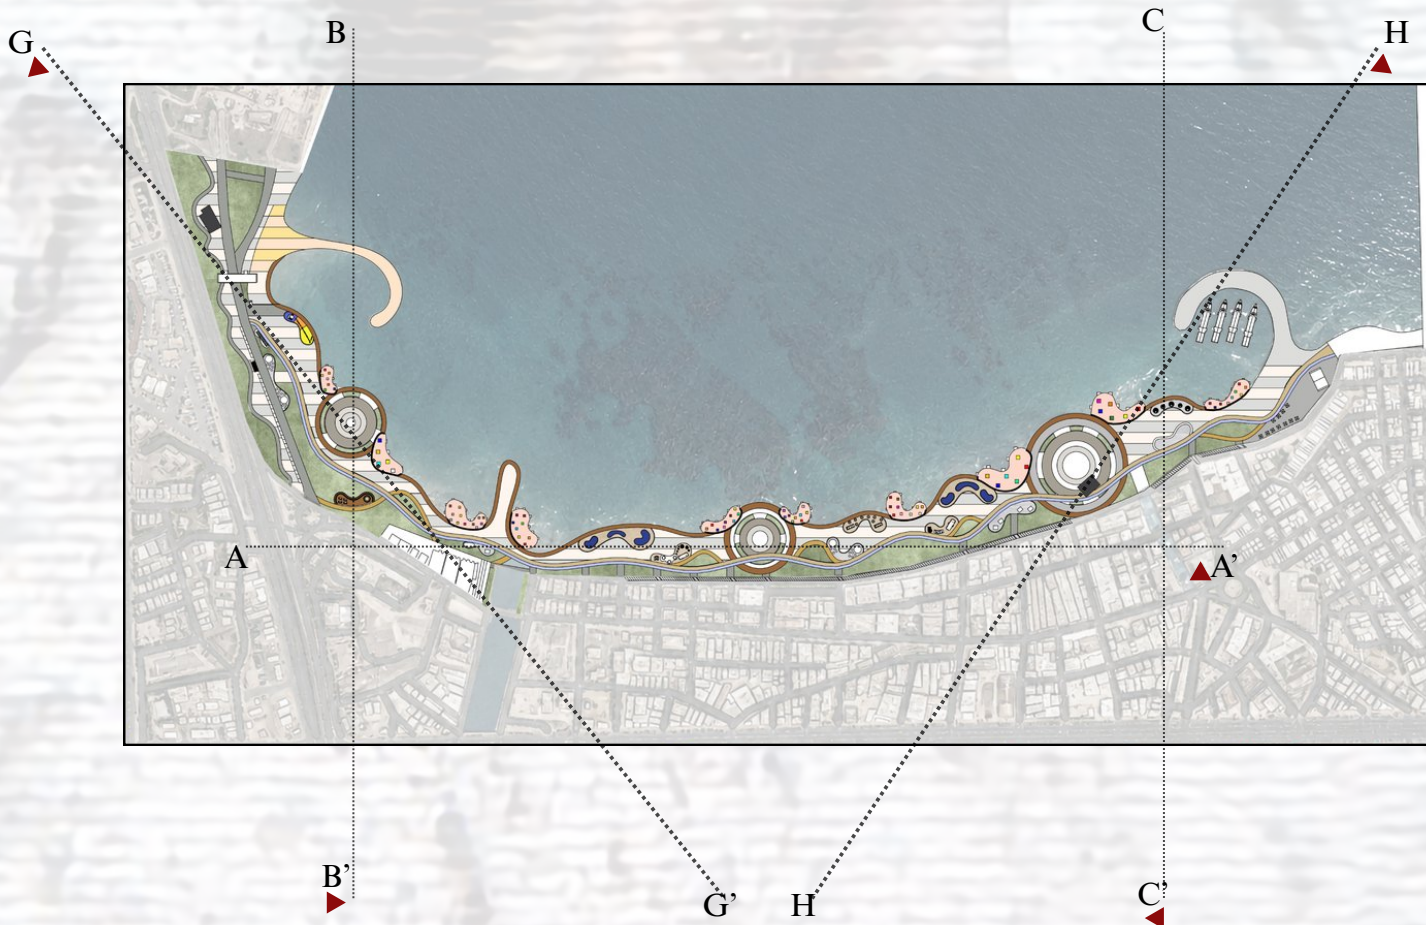

BURSA ULUDAĞ ÜNİVERSİTESİ ZİRAAT FAKÜLTESİ PEYZAJ MİMARLIĞI BÖLÜMÜ
PEYZAJ PROJESİ 5 - GEMLİK KIYI PROJESİ
FİNAL TESLİMİ



BURSA ULUDAĞ ÜNİVERSİTESİ ZİRAAT FAKÜLTESİ PEYZAJ MİMARLIĞI BÖLÜMÜ
PEYZAJ PROJESİ 5 - GEMLİK KIYI PROJESİ
FİNAL TESLİMİ



BURSA ULUDAĞ ÜNİVERSİTESİ ZİRAAT FAKÜLTESİ PEYZAJ MİMARLIĞI BÖLÜMÜ
PEYZAJ PROJESİ 5 - GEMLİK KIYI PROJESİ
FİNAL TESLİMİ



BURSA ULUDAĞ ÜNİVERSİTESİ ZİRAAT FAKÜLTESİ PEYZAJ MİMARLIĞI BÖLÜMÜ
PEYZAJ PROJESİ 5 - GEMLİK KIYI PROJESİ
FİNAL TESLİMİ



BURSA ULUDAĞ ÜNİVERSİTESİ ZİRAAT FAKÜLTESİ PEYZAJ MİMARLIĞI BÖLÜMÜ
PEYZAJ PROJESİ 5 - GEMLİK KIYI PROJESİ
FİNAL TESLİMİ



BURSA ULUDAĞ ÜNİVERSİTESİ ZİRAAT FAKÜLTESİ PEYZAJ MİMARLIĞI BÖLÜMÜ
PEYZAJ PROJESİ 5 - GEMLİK KIYI PROJESİ
FİNAL TESLİMİ




BURSA ULUDAĞ ÜNİVERSİTESİ ZİRAAT FAKÜLTESİ PEYZAJ MİMARLIĞI BÖLÜMÜ

PEYZAJ PROJESİ 5 - GEMLİK KIIYI PROJESİ DETAY PAFTA


FİNAL TESLİMİ

DÖŞEME DETAYLARI


PLAUEN

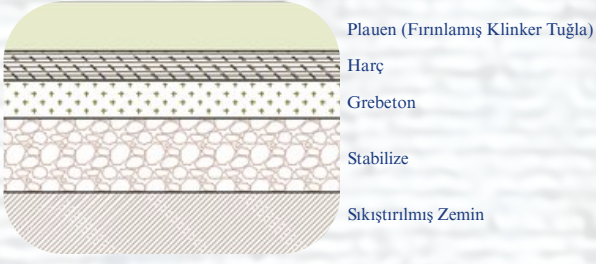


BAZALT

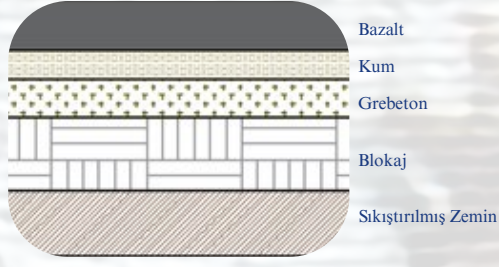




GRANİT KÜP TAŞ

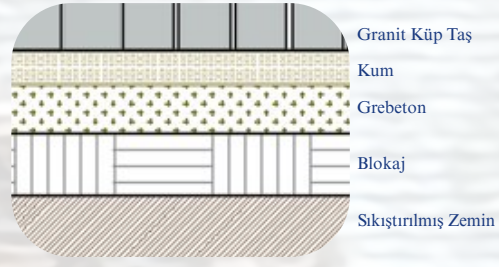




ANDEZİT

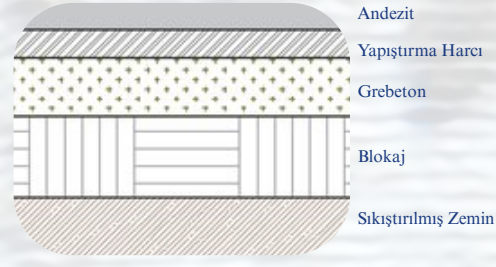





DENİZ HİYARI PLATFORM

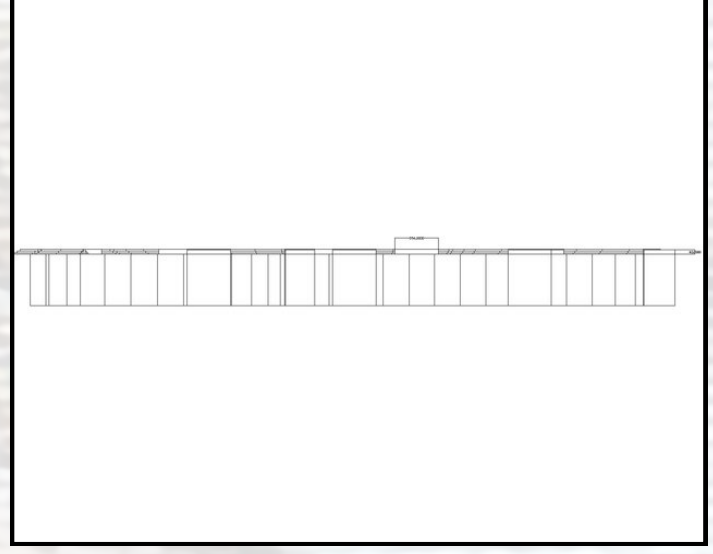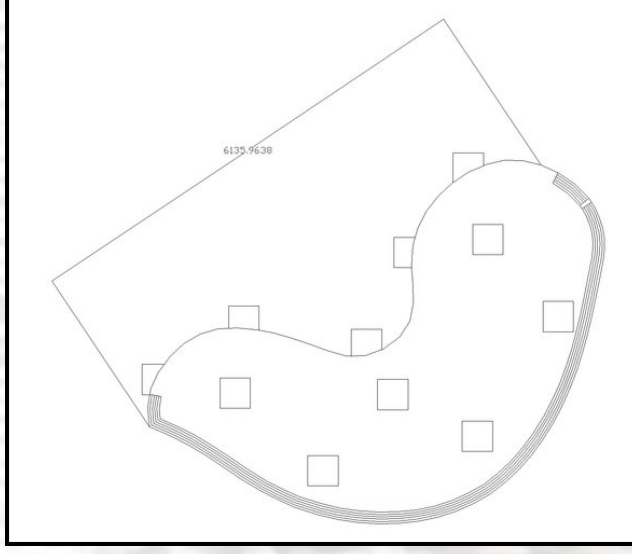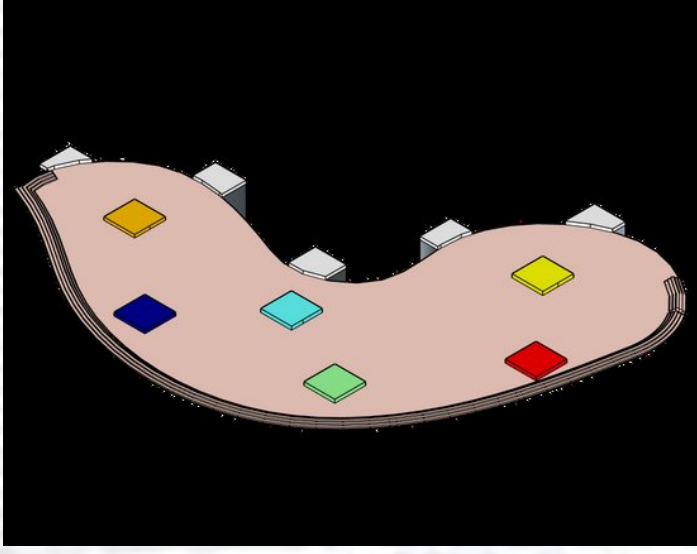



SPOR ALANI

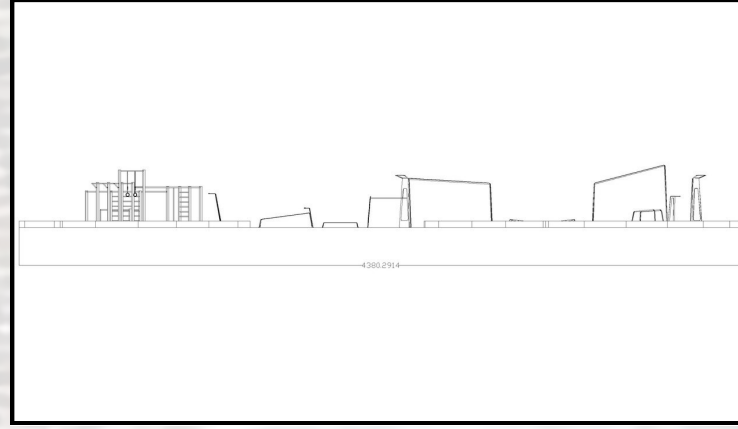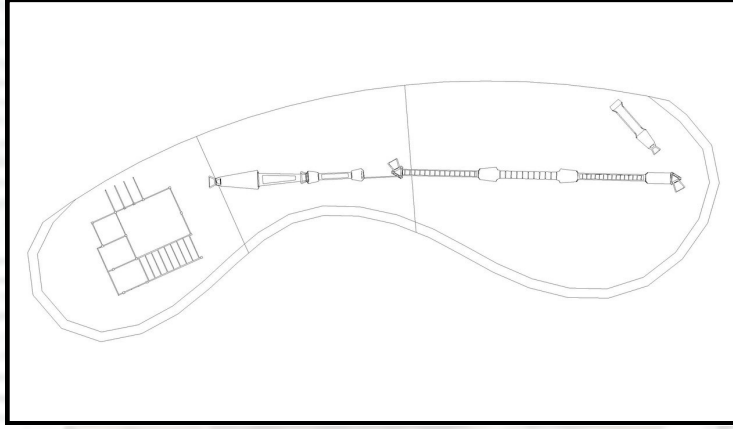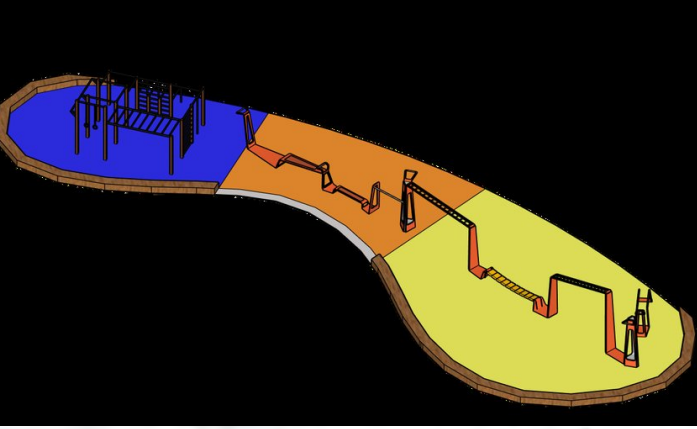

KIYI HAFİZASI ATÖLYESİ

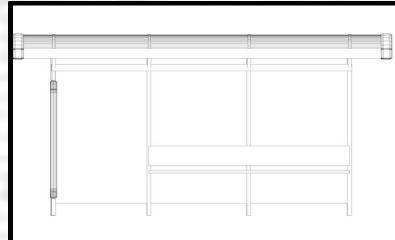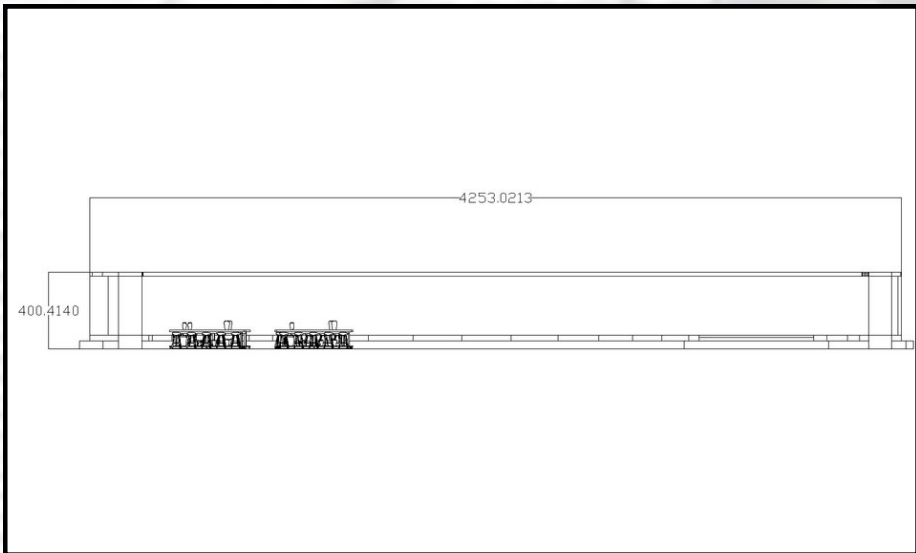
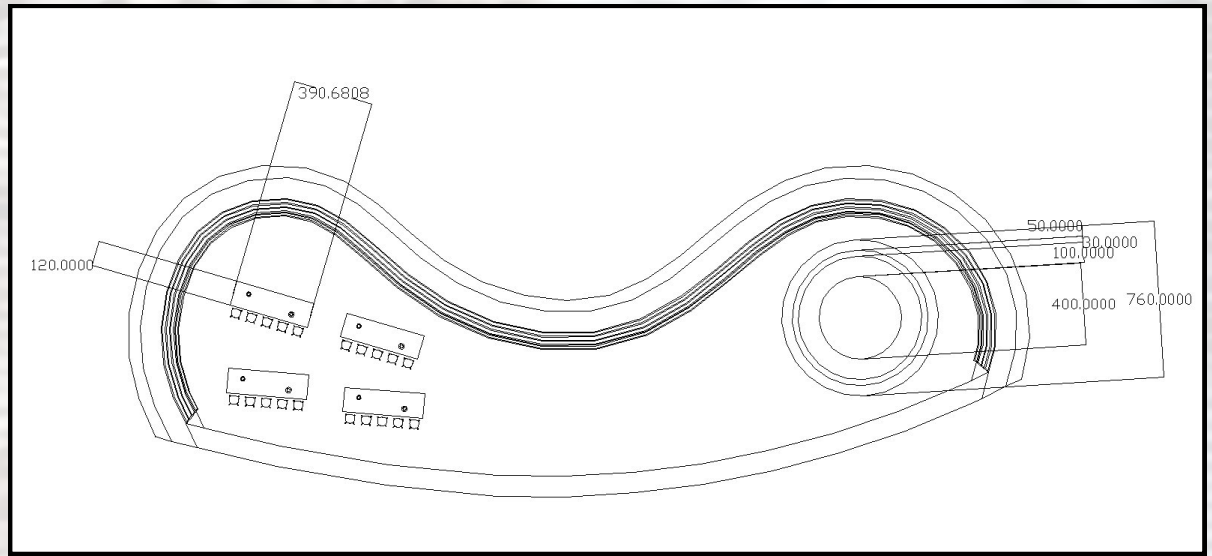
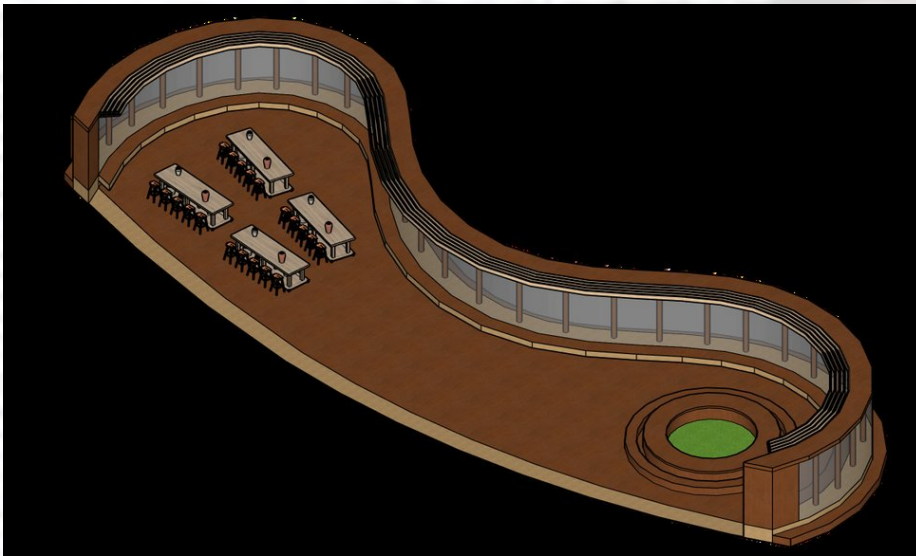


OTOBÜS DURAĞI VE BİSİKLET PARK YERİ





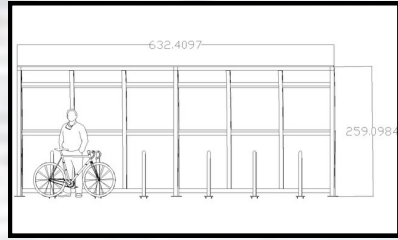
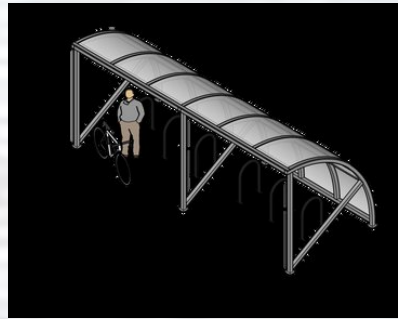


BURSA ULUDAĞ ÜNİVERSİTESİ ZİRAAT FAKÜLTESİ PEYZAJ MİMARLIĞI BÖLÜMÜ
PEYZAJ PROJESİ 5 - GEMLİK KIYI PROJESİ DETAY PAFTA
FİNAL TESLİMİ




DENİZ HİYARI YEMEK STANDI

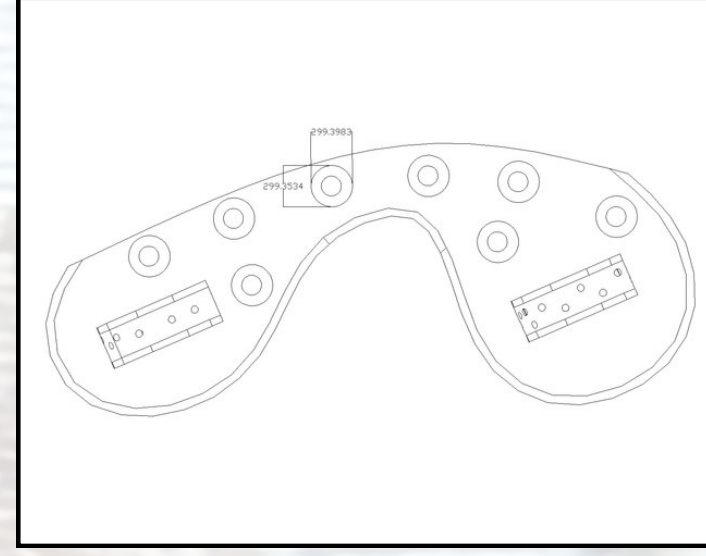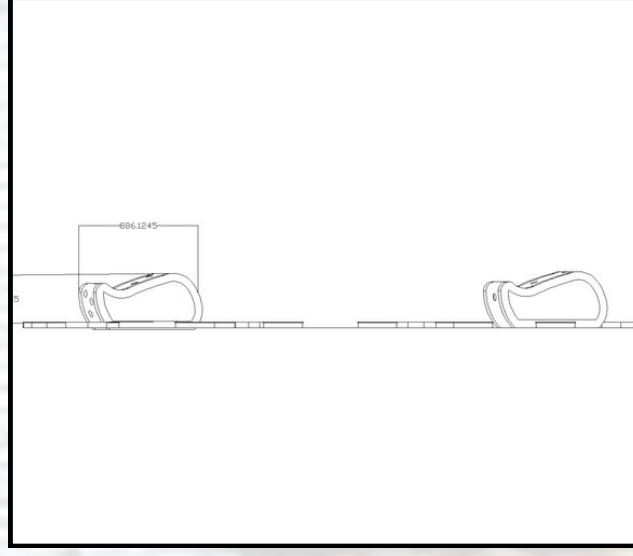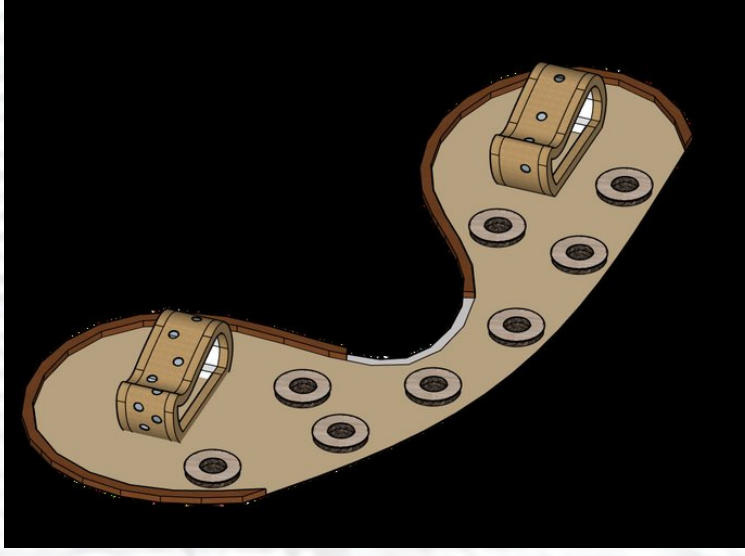

ÇOCUK OYUN ALANI

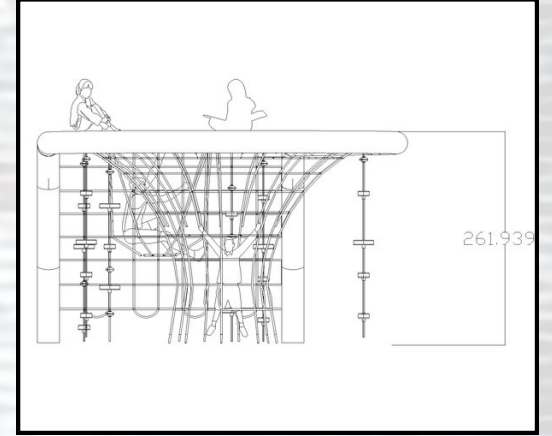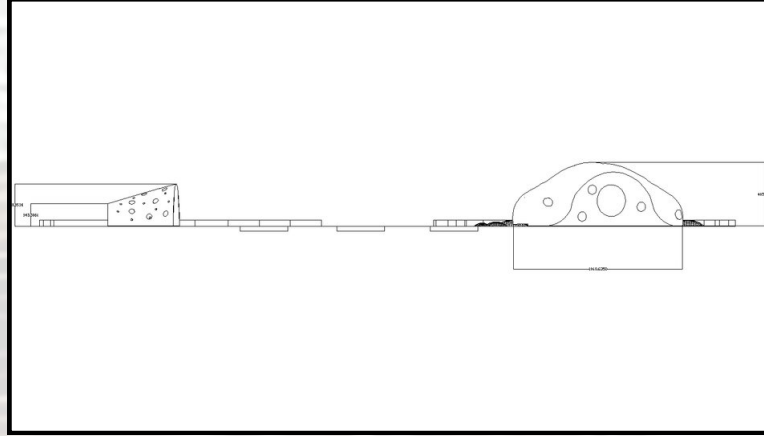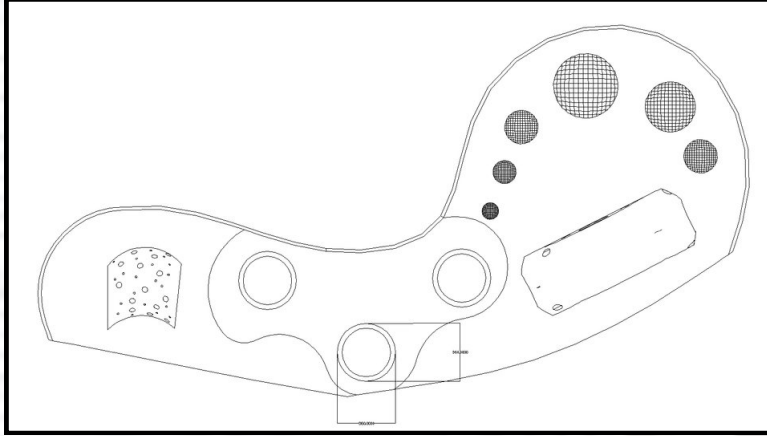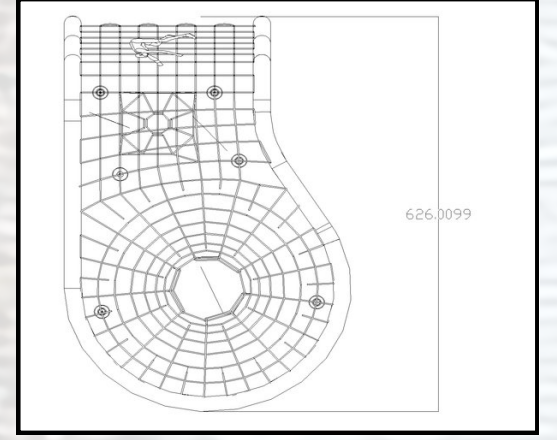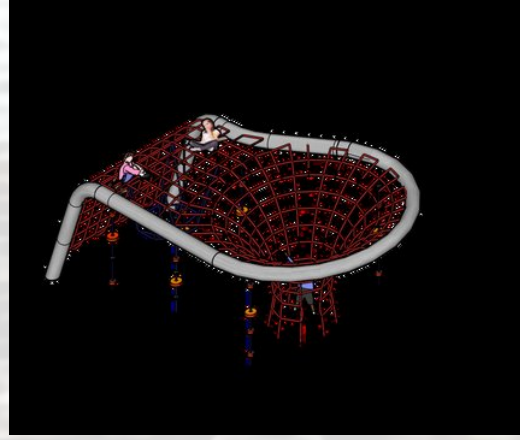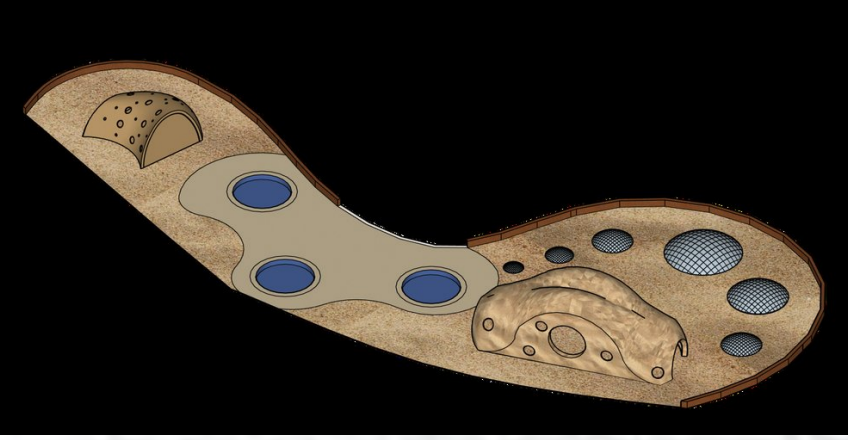

DENİZ HİYARI YETİŞTİRİCİLİK STANDI

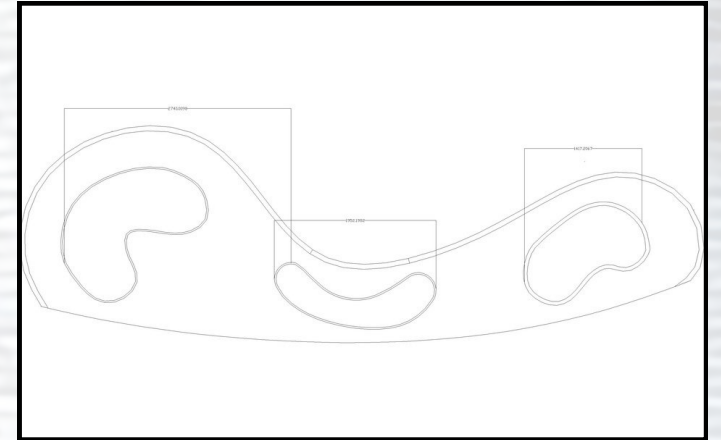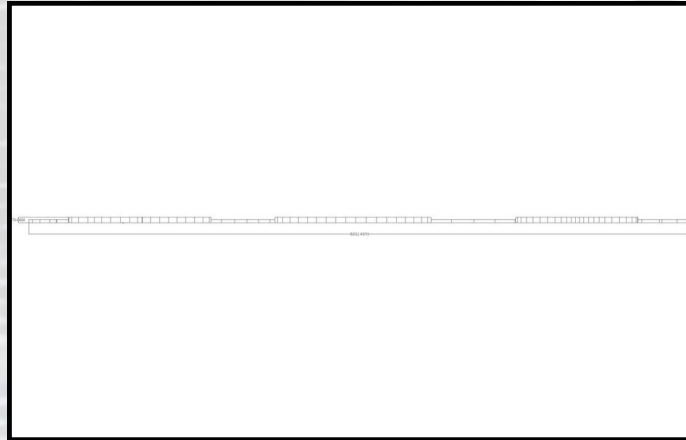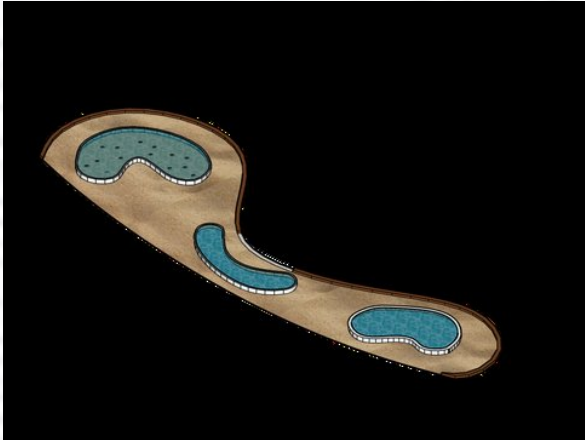

“BUGÜN NEYE MARUZ KALİYORUZ?” NOKTALARI

